

DOOR-WINDOW SCHEDULE

MARK	SIZE	CILL	LINTEL	DESCRIPTION
GL-1	2400 x 2300	100	2400	Glass Window Fixed/Openable
GL-2	2770 x 2300	100	2400	Glass Window Fixed/Openable
GL-3	1150 x 1450	950	2400	Glass Window Openable
GL-4	1460 x 1450	950	2400	Glass Window Openable
GL-5	5700 x 2300	100	2400	Glass Door/Window Fixed/Openable
GL-6,6a,6b	As per site	100	2400	Shower Partition
GL-7	3500 x 2300	100	2400	Glass Door/Window Fixed/Openable
GL-8	3975 x 1100	100		Glass Railing
GL-9	4100 x 2400	100	2400	Glass Window Fixed/Openable
GL-10	1000 x 1450	950	2400	Glass Window Openable
D1	1450 x 2400	00	2400	Flush Door
D2	1000 x 2400	00	2400	Flush Door
D3	800 x 2400	00	2400	Flush Door
D4	As Lift			as per Lift Vendor

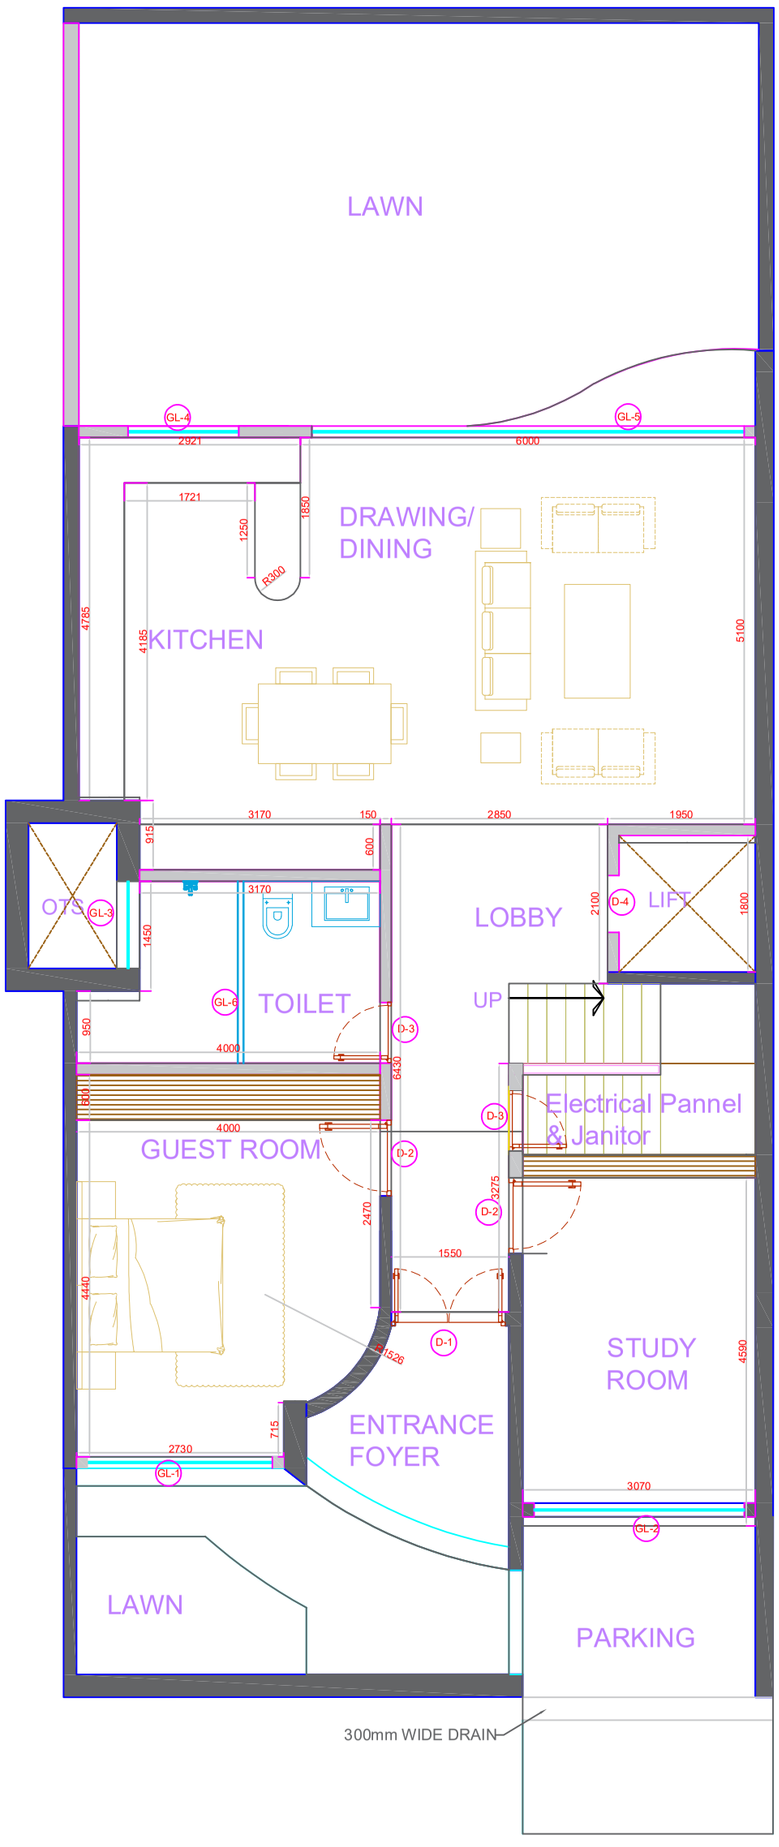

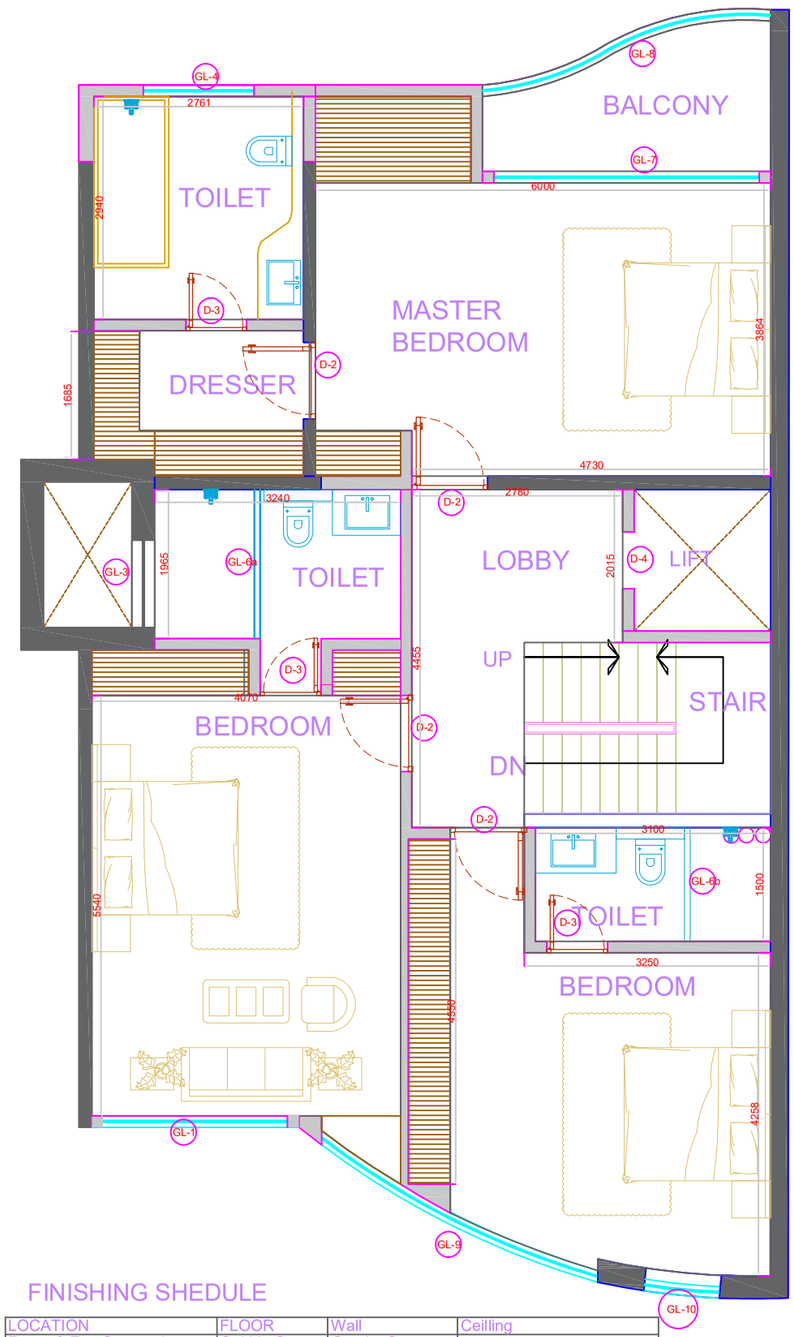

FINISHING SHEDULE

LOCATION	FLOOR	Wall	Ceilling
Ramp & Ext. Coutyard	Cobble Stone	Granite Stone	
Ext. Entrance Area	Granite Stone	Paint Finish	Paint Finish
Entrance Foyer & Lobby	Italian Stone	Veneer Cladding	Veneer Polished
Study Room	Italian Stone	Veneer Cladding	POP Painted
Guest Room	Italian Stone	Paint Finish	POP Painted
Guest Room Toilet	Tile	Tile	POP Painted
Drawing /Dining	Italian Stone	Veneer Cladding	POP Painted/Veneer/Glass
Kitchen	Italian Stone	Italian Stone	POP Painted
Backyard Lawn Sitting Area	Granite Stone	Paint Finish	

CONTRACTOR:-

UNIQUE PROJECT SOLUTIONS

D-53/4, Ground Floor, Shaheen Bagh, Abul Fazal Encl.-2
Jamia Nagar, Okhla, New Delhi 110025
E- uniqueprojectsolutions@gmail.com
M-9911012341

PROJECT :- RENOVATION WORK AT GH-18, CELEBRITY HOMES, PALAM VIHAR GURUGRAM

CLIENT:- Mr. Praveen Kumar Yadav

ARCHITECTS:- Mr. Harish

SHEET CONTENTS :-
GROUND FLOOR PLAN

DRN.	CHD.	DWG. NO. :-
TA	JH	UPS/GH18/PV/001

RELEASED FOR :- ☐PRELIMINARY ☐TENDER ☐INFORMATION ■APPROVAL ☐FABRICATION ☐SERVE

DATE :-17.08.25

SCALE:-NTS

REV.	SHT.NO.
R0	1 of 1